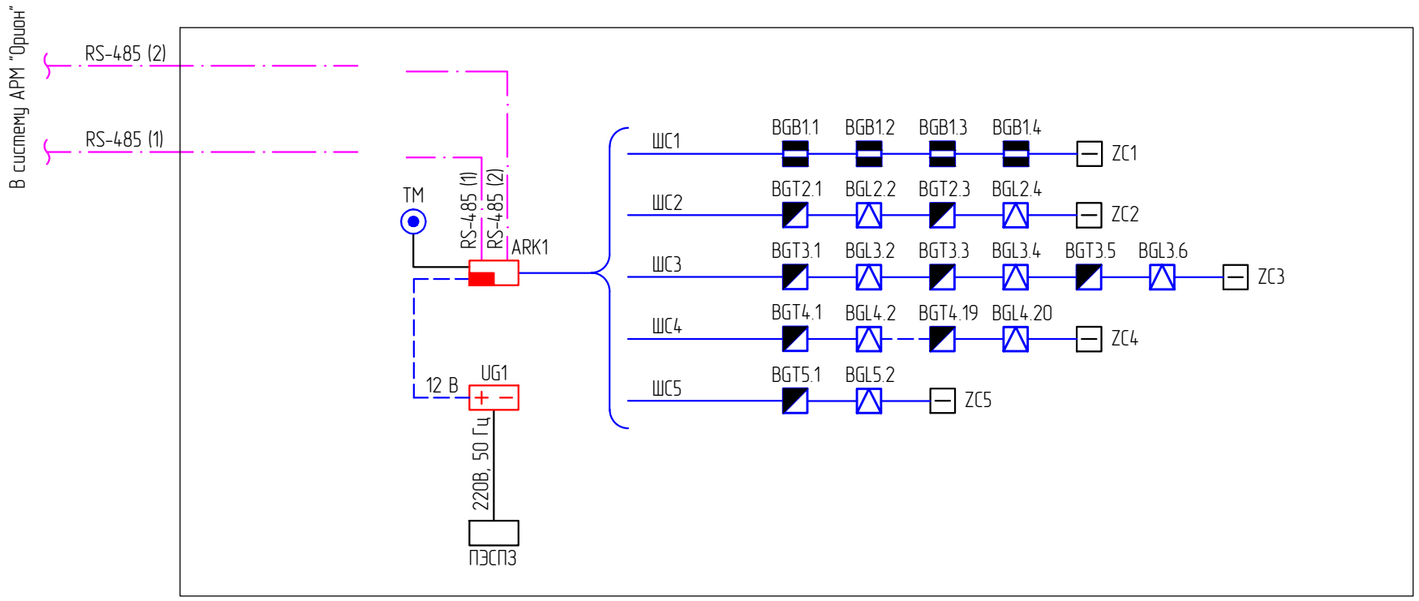



Условные обозначения

Графическое и текстовое обозначение		Наименование оборудования
	ARK	Прибор приемно-контрольный пожарный Сигнал-10 2RS485
	UG	Резервированный источник питания РИП-12 исп. 51
	BGB	Извещатель магнитоконтактный ИО 102-29 "Эстет-Сейф"
	BGT	Извещатель звуковой ИО 329-3 "Арфа"
	BGL	Извещатель оптико-электронный ИО 309-30 " Пирон-Ш"
	ZC	Устройство шлейфовое контрольное Маяк-ШС1
	TM	Порт Touch Memory

Взам. инв. №

Подп. и дата

Инв. № подл.

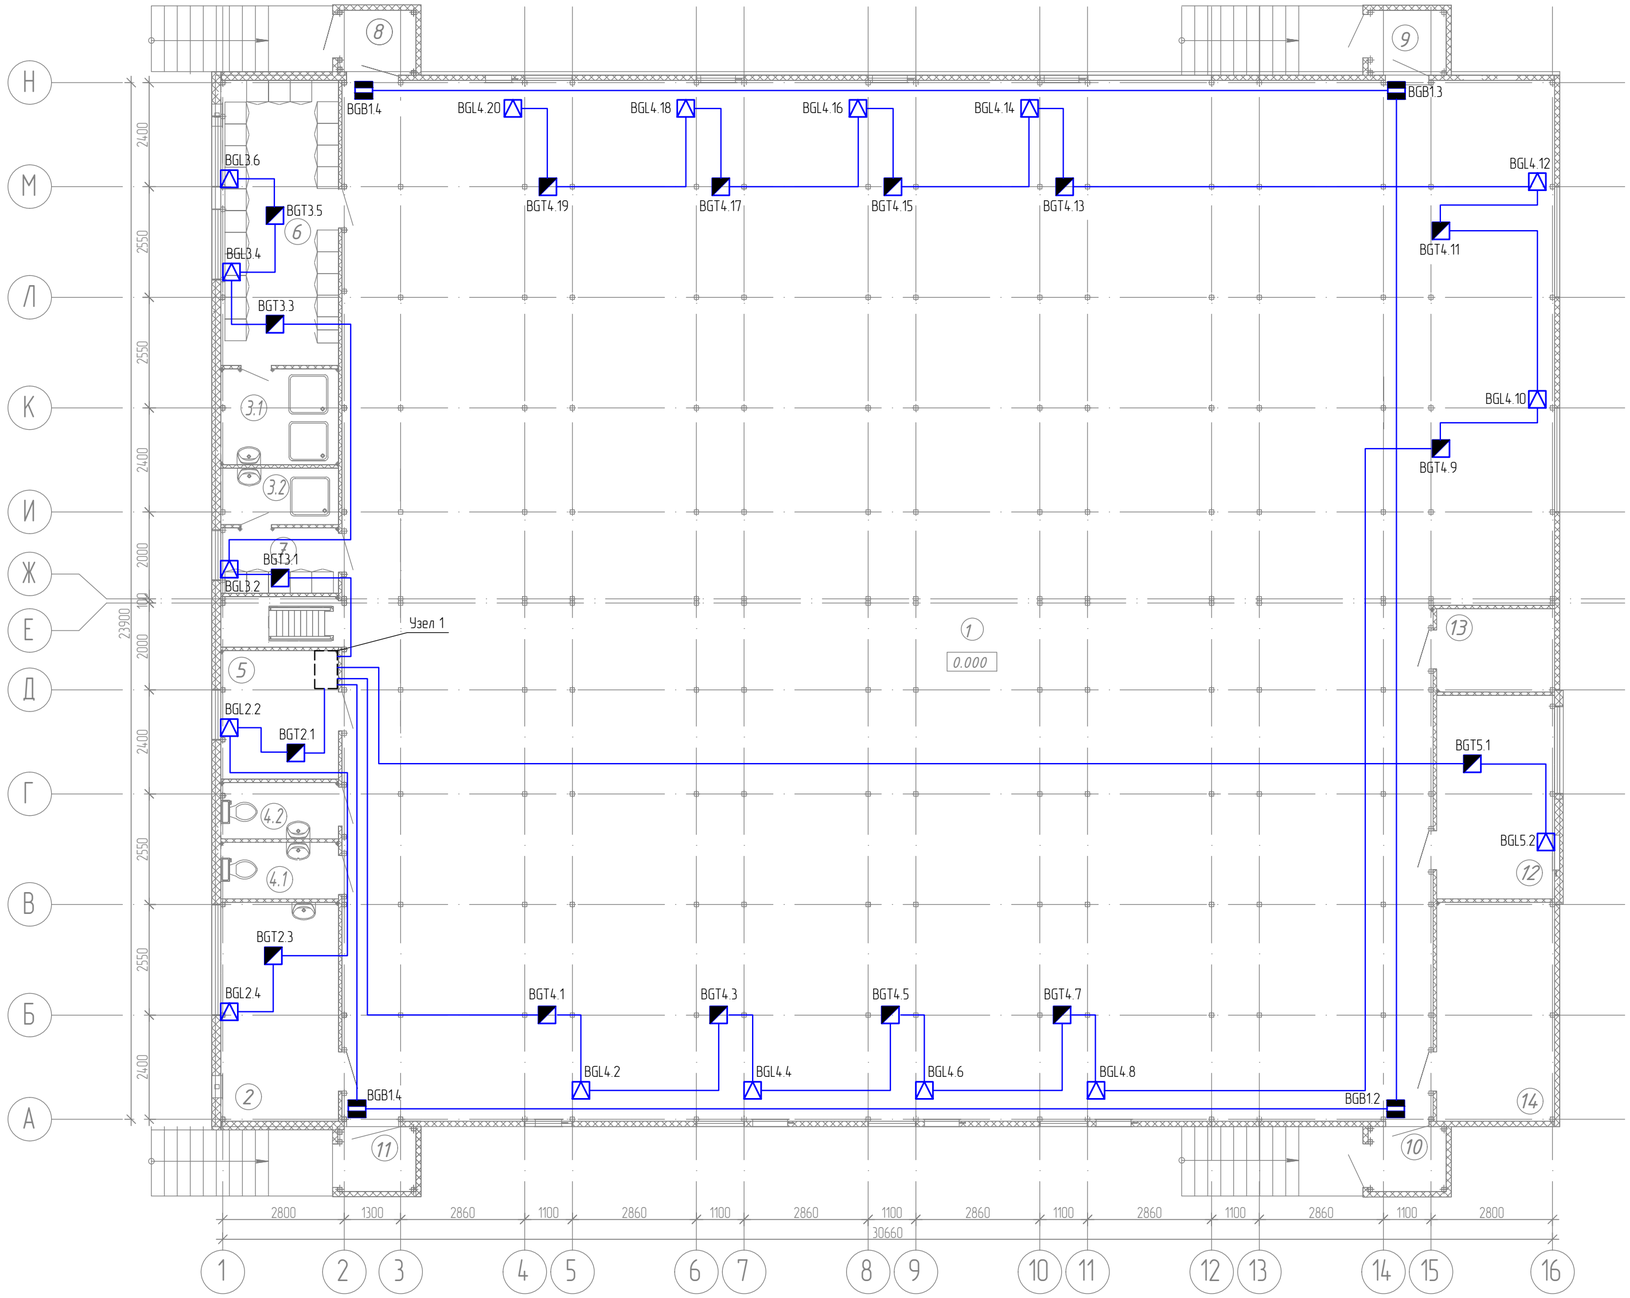

Экспликация помещений

№	Наименование	Площадь, м.кв.	Категория
1	Котельный зал	636,94	Г
2	Комната приема пищи	13,74	Д
3	Душевая	2,16	Д
4	Комната уборочного инвентаря с санузлом	6,97	Д
5	Комната начальника котельной	5,71	Д
6	Гардеробная	25,13	Д
7	Помещение складирования запчастей и инвентаря	6,80	Д
8	Тамбур	2,74	Д
9	Тамбур	2,74	Д
10	Тамбур	2,74	Д
11	Тамбур	2,74	Д
12	Комната обогрева	12,75	Д
13	Подсобное помещение	5,98	Д
14	Электрощитовая	13,74	Д

Условные обозначения

Графическое и текстовое обозначение		Наименование оборудования
	ARK	Прибор приемно-контрольный пожарный Сигнал-10 2RS485
+ −	UG	Резервированный источник питания РИП-12 исп. 51
	BGB	Извещатель магнитоконтактный ИО 102-29 "Эстет-Сейф"
	BGT	Извещатель звуковой ИО 329-3 "Арфа"
	BGL	Извещатель оптико-электронный ИО 309-30 " Пирон-Ш"
	ZC	Устройство шлейфовое контрольное Маяк-ШС1
	TM	Порт Touch Memory

Узел 1



Взам. инв. №

Подп. и дата

Инв. № подл.